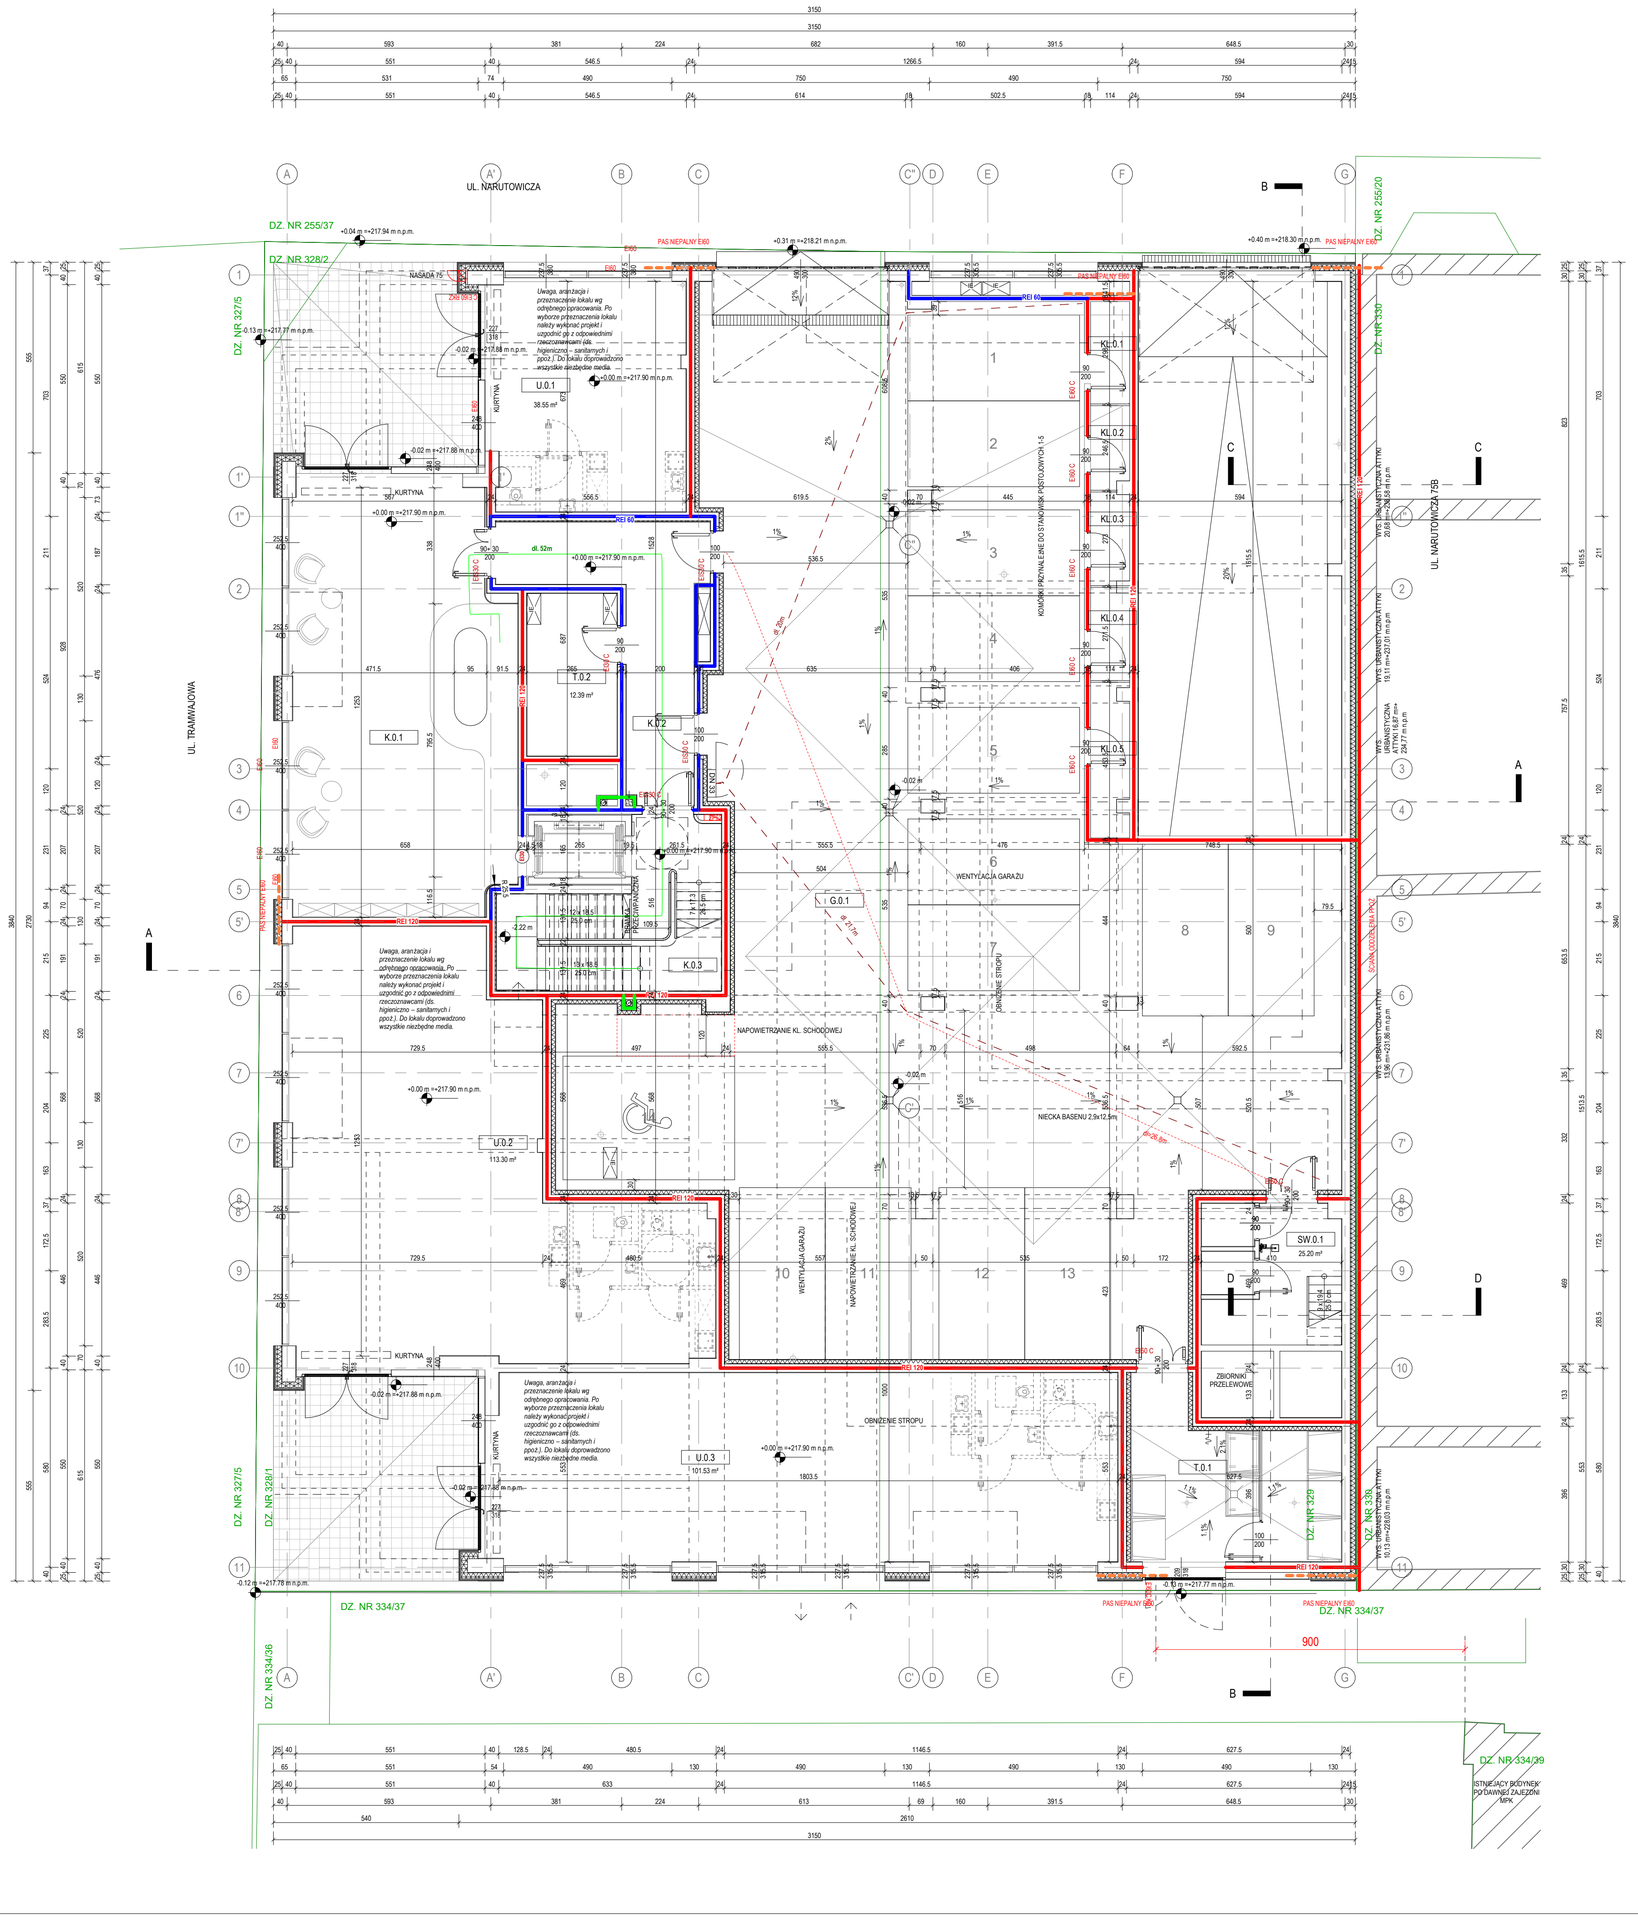


Zestawienie Powierzchni Us ług

Nr lokalu	Nazwa	Powierzchnia
U.0.1	LOKAL USŁUGOWY 1	38.55 m²
U.0.2	LOKAL USŁUGOWY 2	113.30 m²
U.0.3	LOKAL USŁUGOWY 3	101.53 m²
SUMA: 3		253.38 m²

Parter - Pom.Techniczne i Komunikacja

Nr	Nazwa	Powierzchnia
G.0.1	HALA GARAŻOWA	446.41 m²
K.0.1	HOL	80.69 m²
K.0.2	PRZEDSIONEK PPOŻ	23.87 m²
K.0.3	KLATKA SCHODOWA	23.92 m²
KL.0.1	KOMÓRKA LOKATORSKA	3.39 m²
KL.0.2	KOMÓRKA LOKATORSKA	2.70 m²
KL.0.3	KOMÓRKA LOKATORSKA	3.05 m²
KL.0.4	KOMÓRKA LOKATORSKA	3.03 m²
KL.0.5	KOMÓRKA LOKATORSKA	4.86 m²
SW.0.1	PODBASENIE	25.20 m²
T.0.1	POM. GROMADZENIA ODPADÓW	26.14 m²
T.0.2	POM. ELEKTRYCZNE	12.39 m²
12		655.66 m²

LEGENDA:

OZNACZENIA

- ŚCIANY I SŁUPY ŻELBETOWE / ŚCIANY MUROWANE
- ŚCIANY DZIAŁOWE MUROWANE
- IZOLACJA - STYROPIAN
- IZOLACJA - WEŁNA MINERALNA
- LEKKA ŚCIANKA SYSTEMOWA - KOMÓRKI LOKATORSKIE
- ŚCIANY DZIAŁOWE MUROWANE - PRZYKŁADOWA ARANŻACJA
- ŚCIANA SZCZELINOWA WZDŁUŻ GRANICY DZIAŁKI
- DACH ZIELONY/POW. BIOLOGICZNIE CZYNNA
- POWIERZCHNIA UTWARDZONA
- ZAWÓR CZERPALNY
- WPUST PODŁOGOWY
- LINIA ZABUDOWY PIERZEJOWEJ STANOWIĄCEJ PRZEDŁUŻENIE LINII ZABUDOWY ZLOKALIZOWANEJ PRZY UL. NARUTOWICZA 75B
- DONICE
- TARASY/LOGGIE
- -5,37 m — POZIOM WYKOŃCZENIA POSADZKI (dla dachu poziom wierzchu połaci)

OZNACZENIA OKIEN I DRZWI

- SZEROKOŚĆ / WYSOKOŚĆ PRZEJŚCIA
- KIERUNEK OTWIERANIA (PRAWE/LEWE)
- KLASA ODPORNOŚCI OGNIOWEJ DRZWI
- SZEROKOŚĆ / WYSOKOŚĆ OŚCIEŻNICY
- KLASA ODPORNOŚCI OGNIOWEJ OKNA
- KIERUNEK OTWIERANIA (PRAWE/LEWE)
- WYS. PARAPETU OD POZIOMU WYKOŃCZONEJ POSADZKI

OZNACZENIA Z ZAKRESU BEZPIECZEŃSTWA POŻAROWEGO

- PRZEGRODY REI 30 / R 30 / E 30 - zgodnie z opisem na rysunku
- PRZEGRODY EI 60
- PRZEGRODY REI 60
- PRZEGRODY ODDZIELENIA PPOŻ REI 120
- IZOLACJA - WEŁNA MINERALNA
- PRZEJŚCIE EWAKUACYJNE
- ZASIĘG HYDRANTU
- DRZWI / OKNO / ROLETA EI60 - zgodnie z opisem na rysunku
- DRZWI / OKNO / ROLETA EI30 - zgodnie z opisem na rysunku
- DRZWI Z SAMOZAMYKACZEM
- DRZWI DYMOSZCZELNE

UWAGI:

1. NINIEJSZE OPRACOWANIE WYCZERPUJE ZAKRES PROJEKTU BUDOWLANEGO NIEZBĘDNY DO UZYSKANIA POZWOLENIA NA BUDOWĘ. PRZED PRZYSTĄPIENIEM DO PRAC NALEŻY NA PODSTAWIE PROJEKTU BUDOWLANEGO WYKONAĆ OPRACOWANIA PROJEKTÓW TECHNICZNYCH, NIEZBĘDNYCH DLA PRAWIDŁOWEGO PRZEPROWADZENIA PROCESU BUDOWY I FUNKCJONOWANIA BUDYNKU ZGODNIE Z PRZYSZŁYM PRZEZNACZENIEM.
2. PROJEKT NALEŻY ROZPATRYWAĆ ŁĄCZNIE Z OPISEM TECHNICZNYM.
3. W PRZYPADKU STWIERDZENIA ROZBIEŻNOŚCI POMIĘDZY WYŻEJ WYMIENIONYMI OPRACOWANIAMI NALEŻY NATYCHMIAST POWIADOMIĆ PROJEKTANTÓW W CELU USTALENIA OSTATECZNEGO ROZWIĄZANIA.
4. WSZYSTKIE WYMIARY POWINNY ZOSTAĆ SPRAWDZONE PRZEZ WYKONAWCĘ PRZED ROZPOCZĘCIEM ROBÓT BUDOWLANYCH. W CELU WYJAŚNIENIA EWENTUALNYCH WĄTPLIWOŚCI NALEŻY ZWRÓCIĆ SIĘ DO PROJEKTANTA.
5. WSZELKIE ROZBIEŻNOŚCI I ZMIANY WYNIKŁE W TRAKCIE BUDOWY NALEŻY UZGADNIAĆ Z PROJEKTANTEM.
6. W PROJEKCIE WYMIARY OTWORÓW DRZWIOWYCH PODANE SĄ W ŚWIETLE PRZEJŚCIA PO OTWARCIU DRZWI. OTWORY POD MONTAŻ STOLARKI (ŚLUSARKI DRZWIOWEJ) WYKONAĆ ZGODNIE Z ZALECENIAMI PRODUCENTA DRZWI WYBRANEGO NA ETAPIE REALIZACJI.
7. UŻYTE MATERIAŁY I URZĄDZENIA POWINNY POSIADAĆ WSZYSTKIE WYMAGANE ATESTY I APROBATY.
8. ŚCIANKI SZACHTÓW INSTALACJI RUROWYCH I KABLOWYCH POWINNY BYĆ ZAMUROWANE PO UŁOŻENIU INSTALACJI.
9. WYKOŃCZENIE MIESZKAŃ PO STRONIE NABYWCÓW LOKALI.
10. WYMIARY WEWNĘTRZNE PODANO W ŚWIETLE KONSTRUKCJI ŚCIAN, BEZ UWZGLĘDNIENIA TYNKÓW.
11. POWIERZCHNIE PODANO Z UWZGLĘDNIENIEM TYNKÓW.
12. NA RYSUNKACH PODANO MINIMALNE KLASY ODPORNOŚCI OGNIOWEJ ELEMENTÓW ODDZIELENIA PRZECIWPOŻAROWEGO. PRZY USTALANIU OSTATECZNEJ KLASY PRZEGRÓD BUDOWLANYCH NALEŻY UWZGLĘDNIĆ WYMAGANIA § 216. 1. WARUNKÓW TECHNICZNYCH, ODPOWIEDNIO DLA KLASY ODPORNOŚCI POŻAROWEJ BUDYNKU - ZGODNIE Z OPISEM TECHNICZNYM WARUNKÓW OCHRONY PRZECIWPOŻAROWEJ.

Rew.	Opis	Data
11	Koordynacja IS 19.10.2026	19.10.2026
8	BasenComplex	5.10.2026
6	Koordynacja konstrukcja 25.09	25.09.2026
5	Koordynacja konstrukcja 18.09	16.09.2026

DESIGN LAB GROUP

BUDOWA BUDYNKU MIESZKALNEGO WIELORODZINNEGO Z CZĘŚCIĄ USŁUGOWĄ WRAZ Z ZAGOSPODAROWANIEM TERENU I NIEZBĘDNYMI URZĄDZENIAMI BUDOWLANYMI W ŁODZI PRZY UL. NARUTOWICZA 75A

ADRES INWESTYCJI:	UL. NARUTOWICZA 75A, 90-132 ŁÓDŹ DZ. EW. NR 328/1, 328/2, 329, 334/36, 334/37, 334/38 OBR EB S-2
INWESTOR:	UNIQUM 5 SP. Z O.O. UL. GDAŃSKA 130, 90-520 ŁÓDŹ
JEDNOSTKA PROJEKTOWA:	DESIGN LAB GROUP POLAND SP. Z O.O. ŁÓDŹ 90-265, UL. ANDRZEJA STRUGA 2
GŁÓWNY PROJEKTANT:	mgr inż. arch. Maciej Taczalski UPR. BUD. W SPEC. ARCH. B. O. NR 49/LOOKK/2014
SPRAWDZAJĄCY:	mgr inż. arch. Bartosz Kaciupski UPR. BUD. W SPEC. ARCH. B. O. NR 09/LOOKK/2019
WSPÓŁPRACA PROJEKTOWA:	mgr inż. arch. Karolina Taczalska mgr inż. arch. Paulina Jaklewicz mgr inż. arch. Natalia Mostowska mgr inż. arch. Jacek Jastrzębski-Lewicki

DATA:	GRUDZIEŃ 2025	NR REWIZJI:
BRANŻA:	ARCHITEKTURA	11
STADIUM:	PROJEKT BUDOWLANY	
SKALA:	1 : 100	NR RYSUNKU:
TYTUŁ RYSUNKU:	RZUT PARTERU	N75A-PB-AR-101